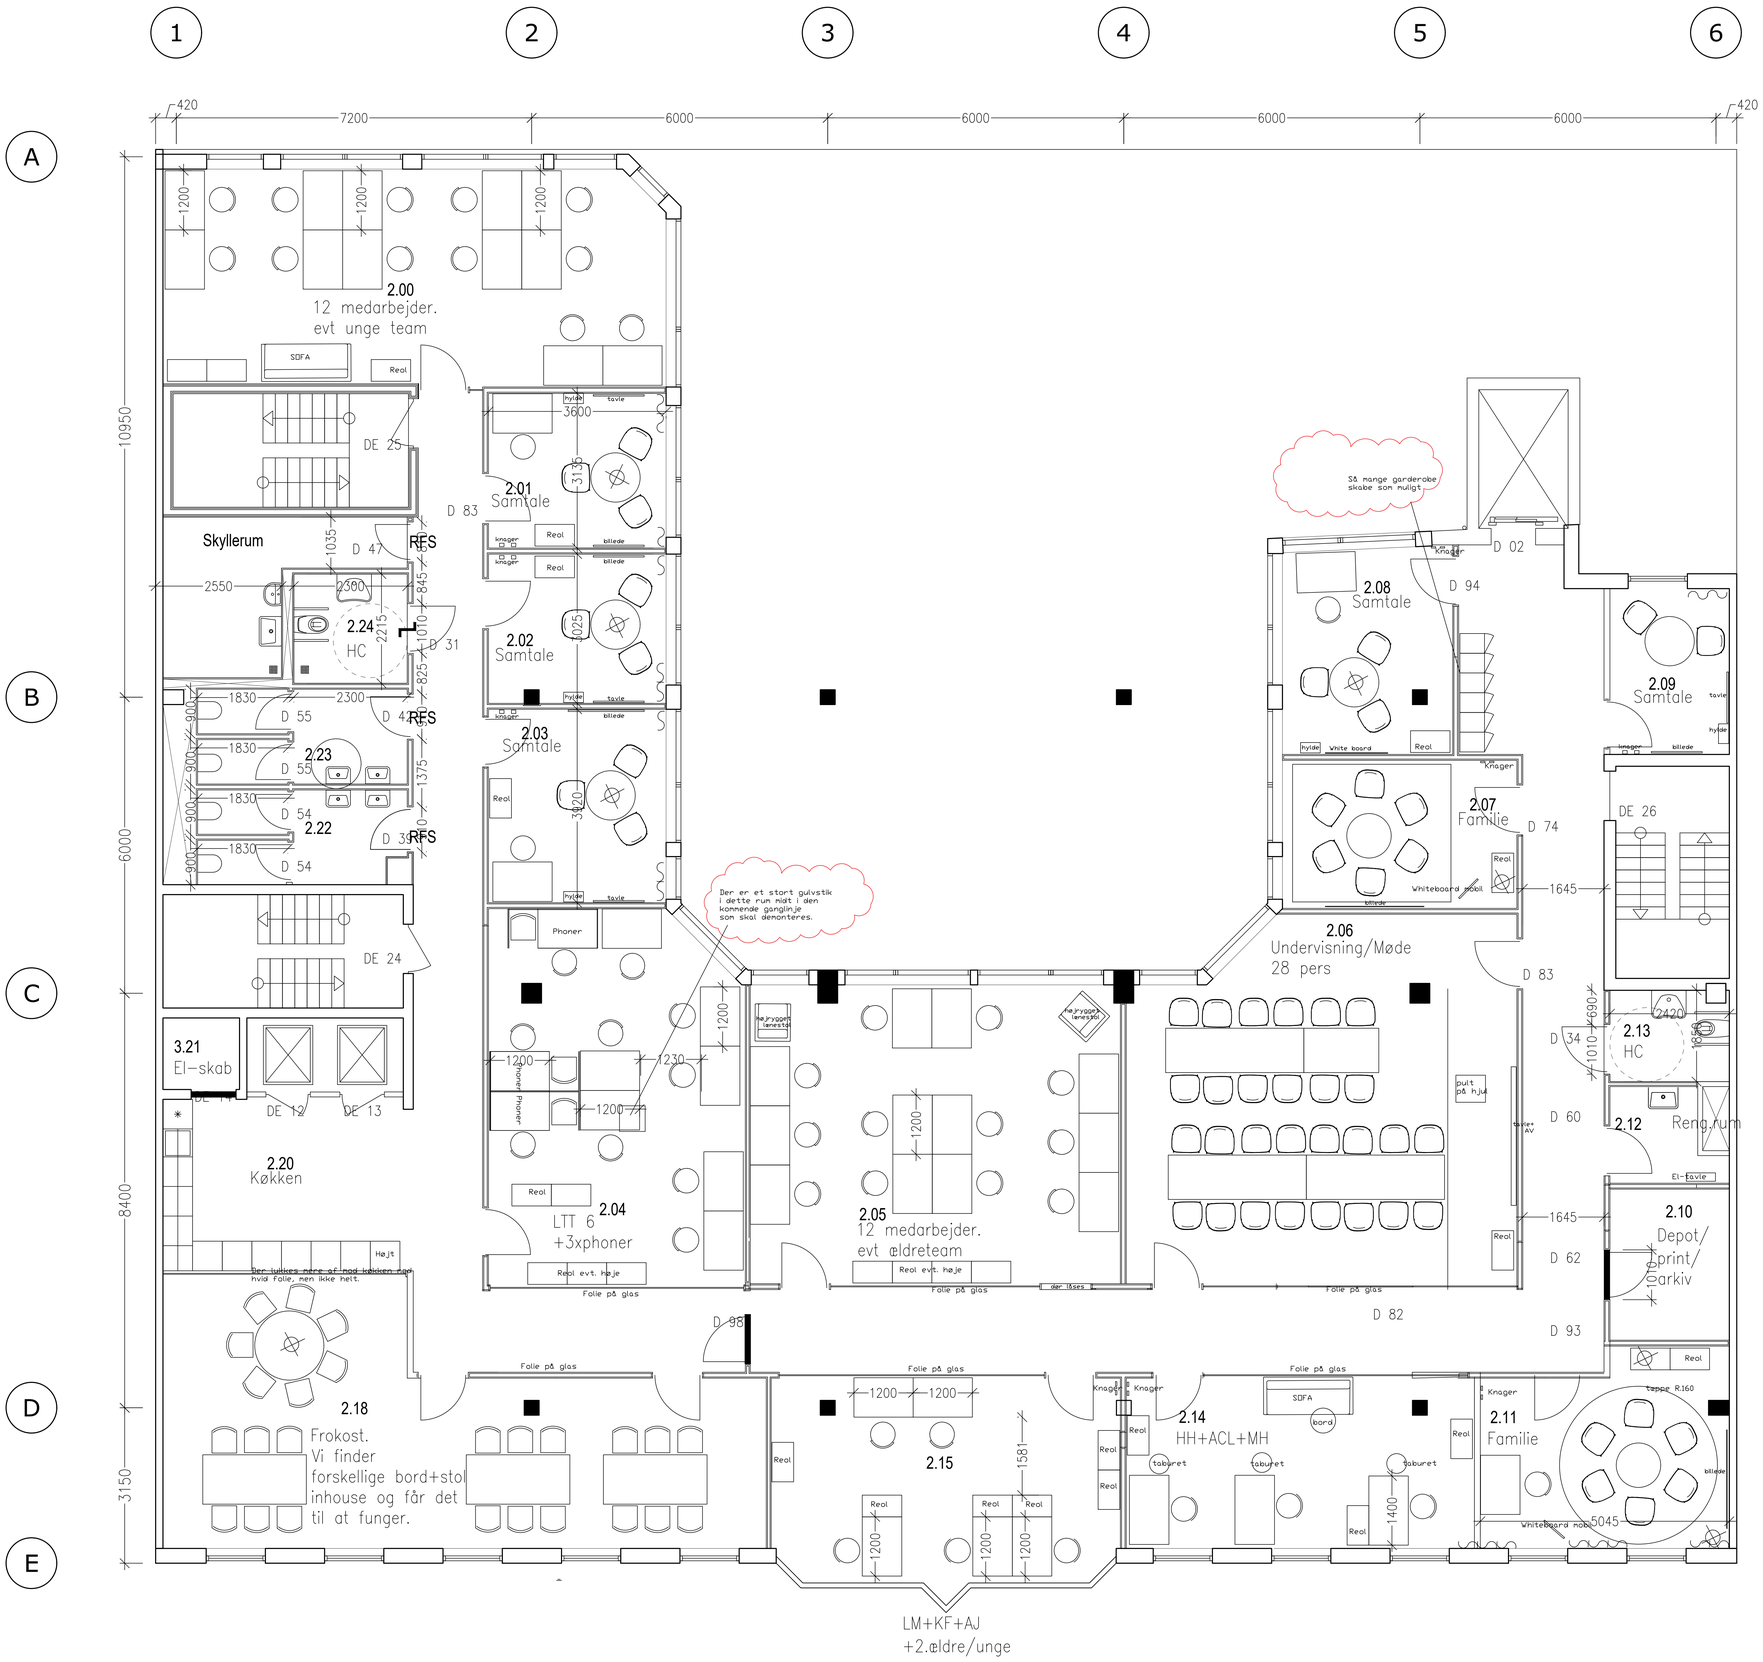

Center for Mental Sundhed – 2.SAL
Vesterbrogade 121.
Ca. 650M2 – 26.02 2025
Indretning af Tinne Ottosen – 28193914