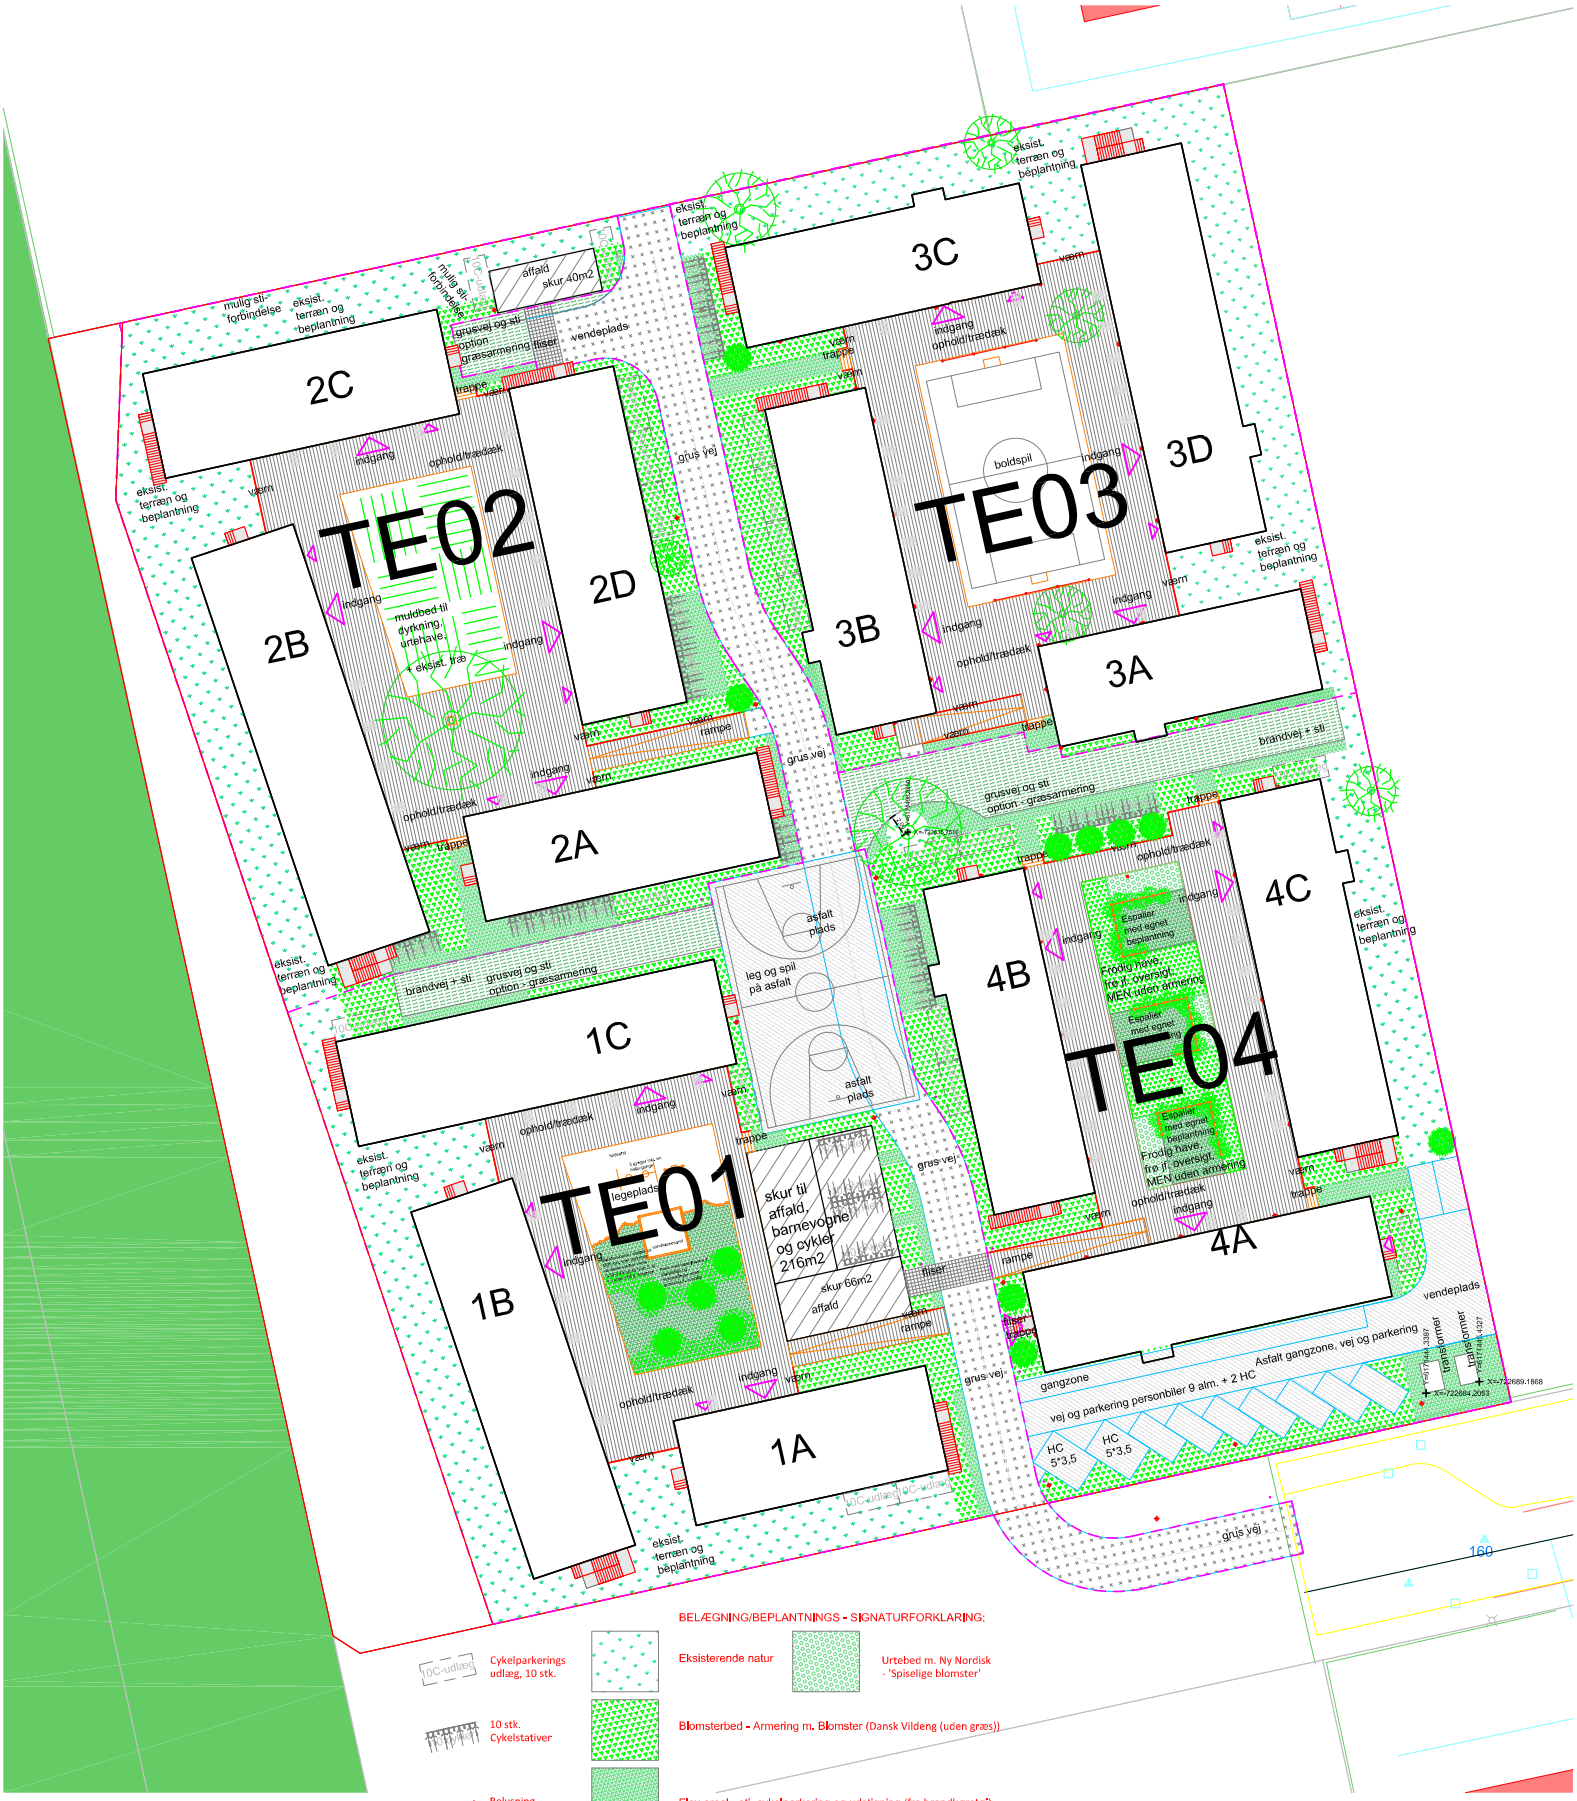

BELÆGNING/BEPLANTNINGS - SIGNATURFORKLARING:

- 10C-udlæg — Cykelparkerings udlæg, 10 stk.
- 10 stk. Cykelstativer
- Belysning, se belysningsplan
- indgang — Hoveddør, indgang
- Mulig indgang til fællesrum
- Rumdeler, ophold og grønt.
- 3 stk. Espalier som på plan, 180 cm højt. med egnet beplantning
- Eksisterende natur
- Blomsterbed - Armering m. Blomster (Dansk Vildeng (uden græs))
- Flex areal - sti, cykelparkering og udstigning (fra brandkøretøj) Armering m. Græs og Blomster (Overdrevsmix)
- Brandvej og sti: jævnt leret vejgrus Option: *armering m. Græs og Blomster* (Overdrevsmix)
- Vej og brandvej: jævnt leret vejgrus
- Boldbane, parkering, gangzone og vej: Asfalt med Thermo-plast
- Betonfliser ved og i skure + indgangsparti ved Fælleshus
- Træ-dæk, -trapper og -ramper
- Urtebed m. Ny Nordisk - 'Spiselige blomster'

N

Boliger til fordrevne ved Bådehavnsgade			TL_100
Emne: LANDSKABSPLAN	Dato.: 2023-03-24	Sagsnr.: 0389	
	Skala: Ikke i skala	Udf.: SCM	
	Fase: udbudsprojekt	Godk.: LJ	
	Model#: 0389_ML_BÅDEHAVNSGADE_UTM32	UTM32	
Arkitekt + Landskab: SLETH A/S	Orientkig 4, 2150 Nordhavn	0045 3213 1001	