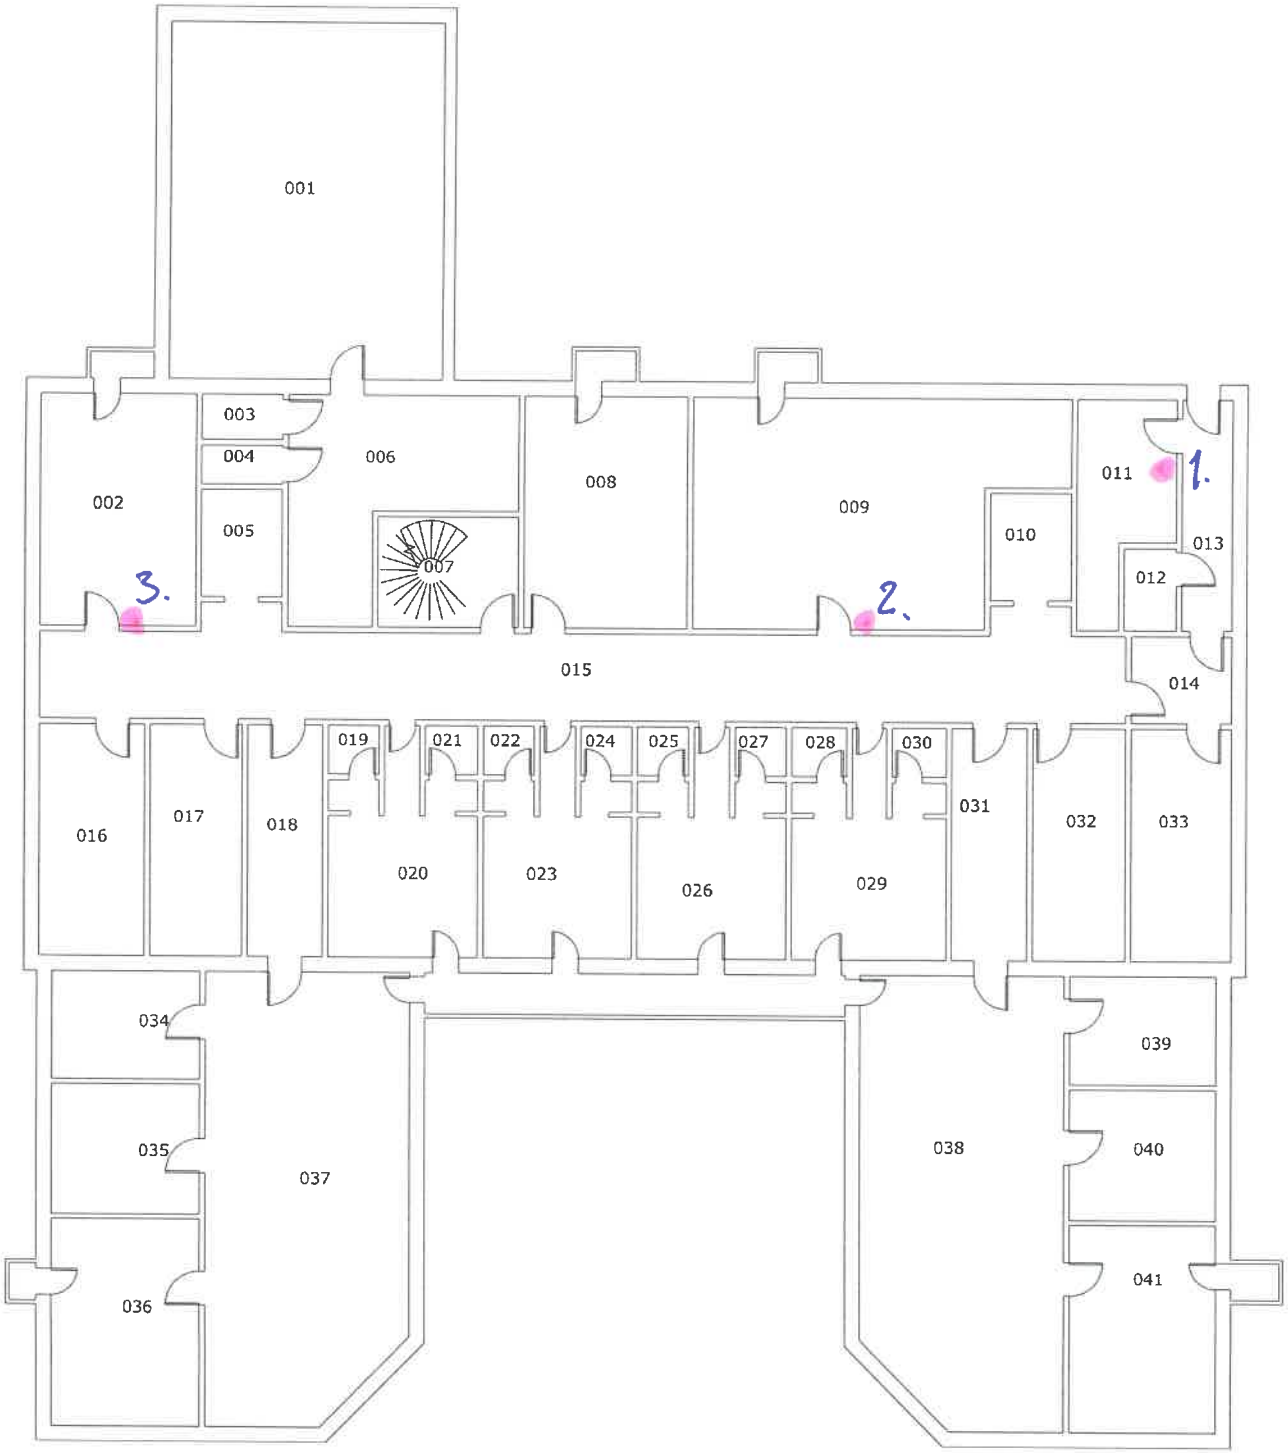
001
002
1.
2.
3.

Kælder

บอกชั้น

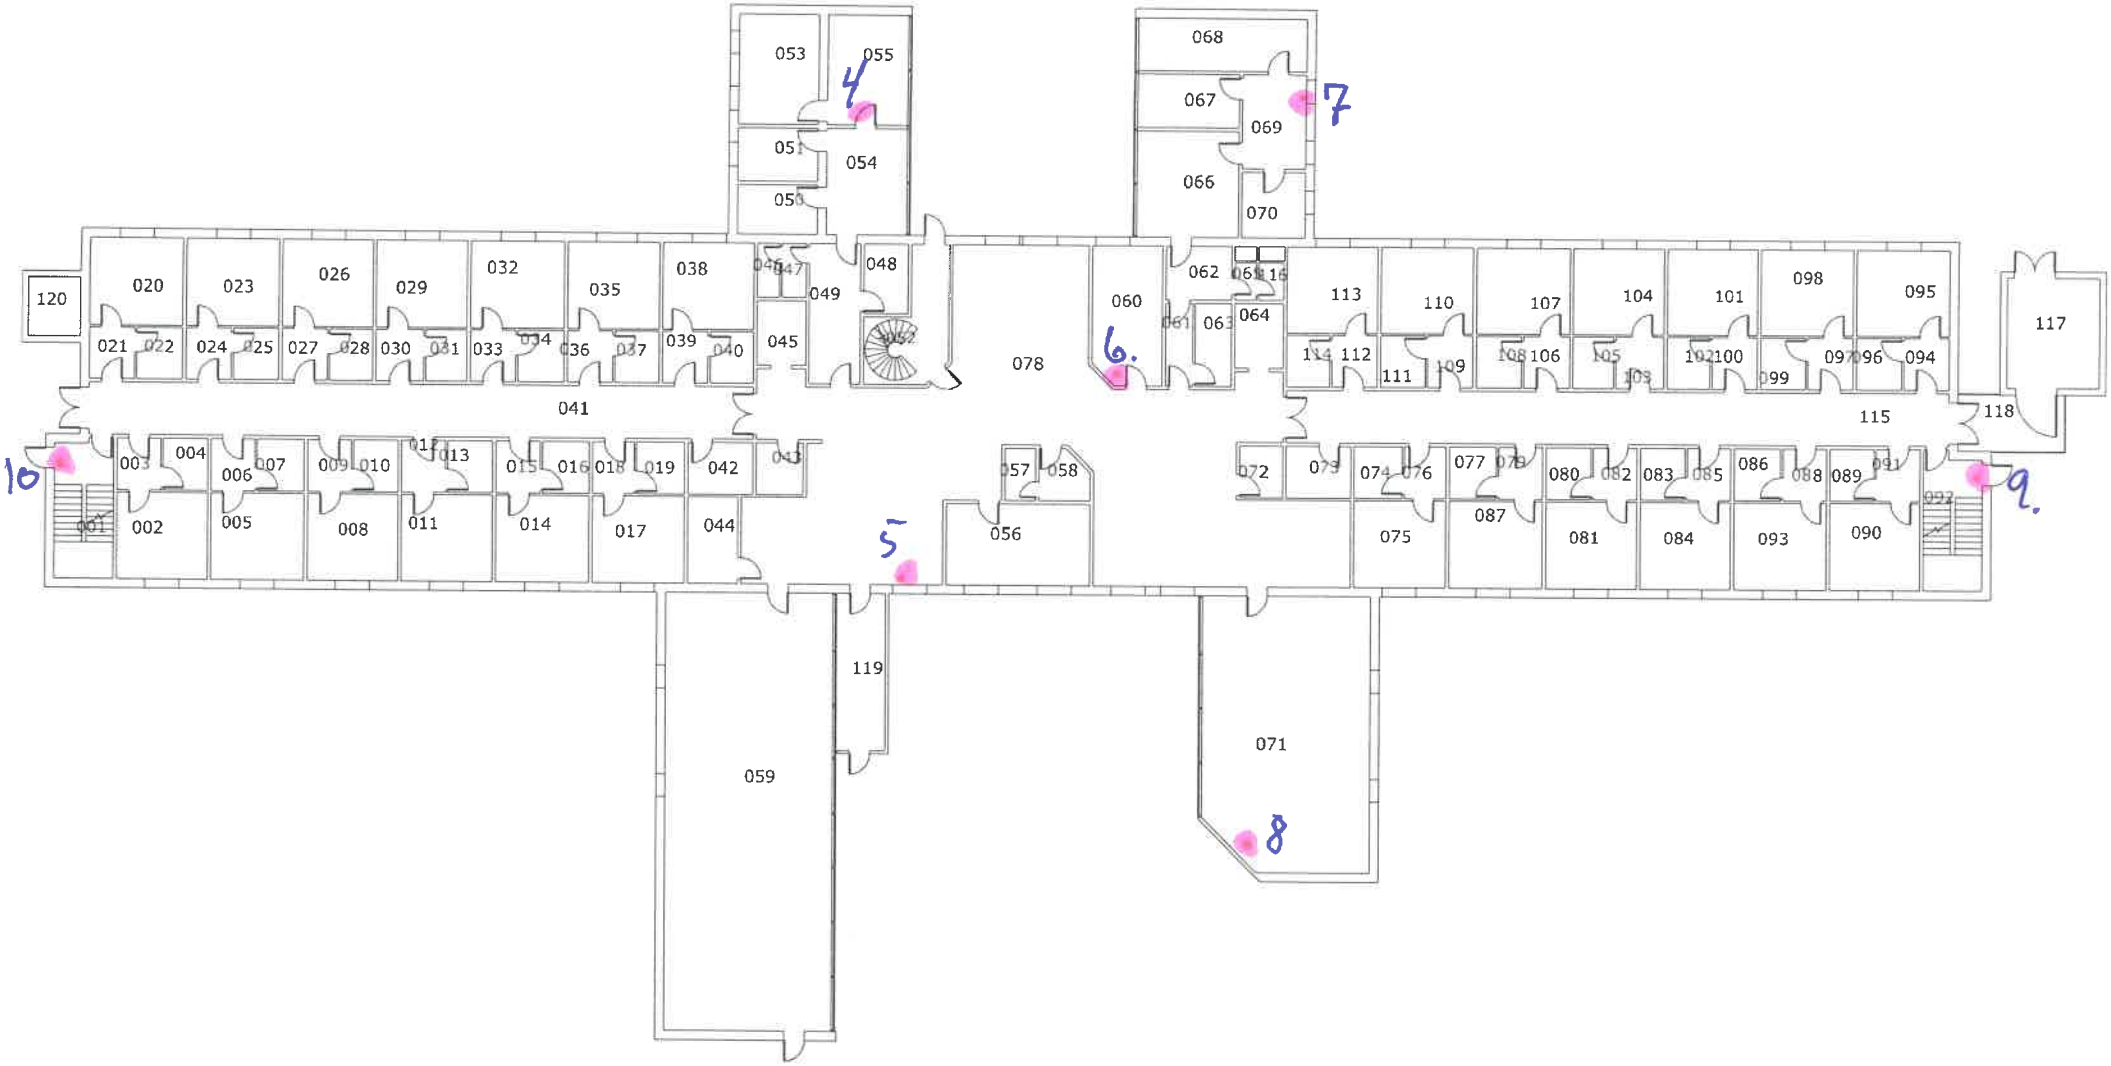
053
055
4
051
054
050
068
067
069
7
066
070
120
020
023
026
029
032
035
038
046
047
049
048
060
062
064
113
110
107
104
101
098
095
117
021
022
024
025
027
028
030
031
033
034
036
037
039
040
045
052
078
6.
061
063
114
112
111
109
108
106
105
103
102
100
099
097
096
094
041
115
118
10
003
004
006
007
009
010
012
013
015
016
018
019
042
043
057
058
072
073
074
076
077
079
080
082
083
085
086
088
089
091
092
9.
001
002
005
008
011
014
017
044
056
5
075
087
081
084
093
090
119
059
071
8

1. sol

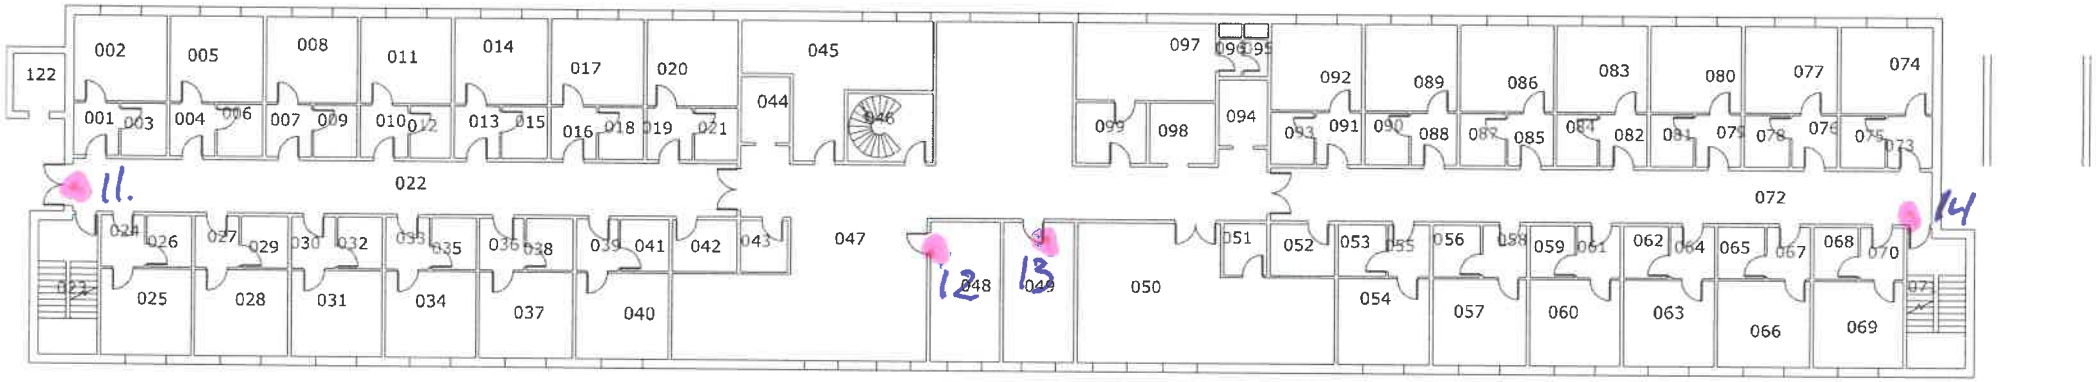
122
002
005
008
011
014
017
020
045
097
092
089
086
083
080
077
074
044
094
099
098
022
072
047
051
052
053
056
059
062
065
068
025
028
031
034
037
040
048
050
054
057
060
063
066
069
11.
12
13
14

2.521

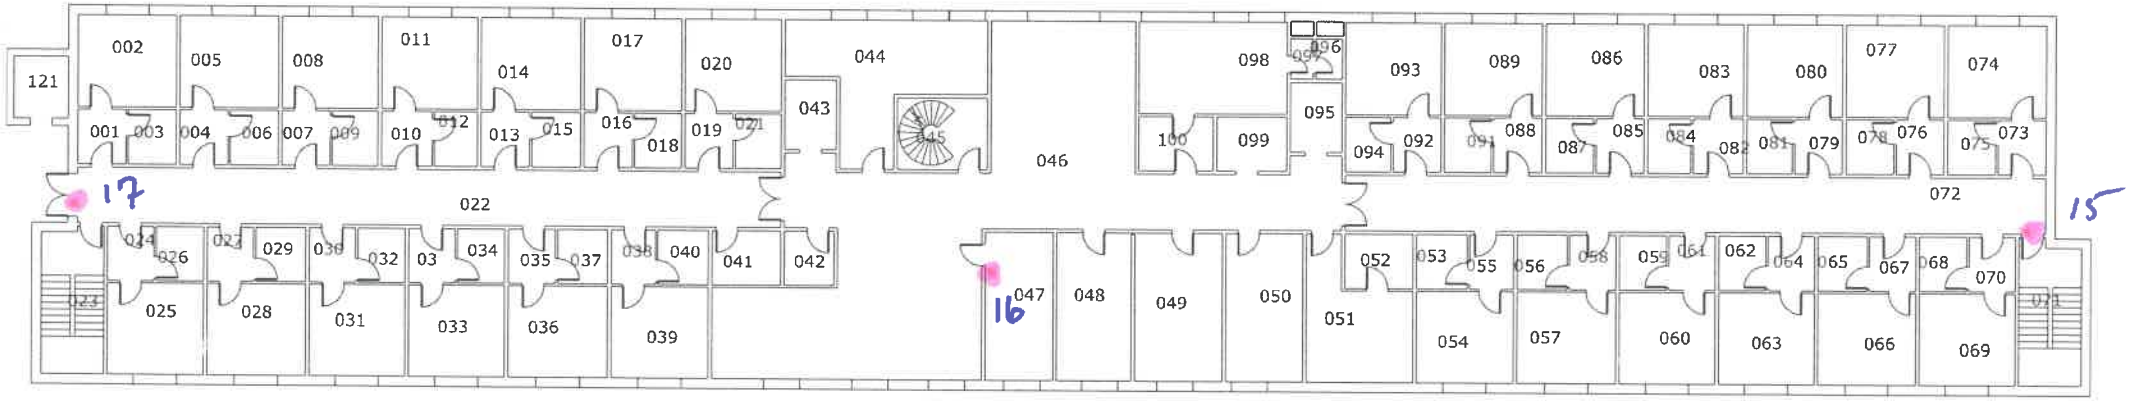
121
002
005
008
011
014
017
020
044
098
097
096
093
089
086
083
080
077
074
001
003
004
006
007
009
010
012
013
015
016
018
019
021
043
045
046
100
099
095
094
092
091
088
087
085
084
082
081
079
078
076
075
073
17
022
072
15
024
026
023
029
030
032
03
034
035
037
038
040
041
042
047
048
049
050
052
053
055
056
058
059
061
062
064
065
067
068
070
025
028
031
033
036
039
16
051
054
057
060
063
066
069

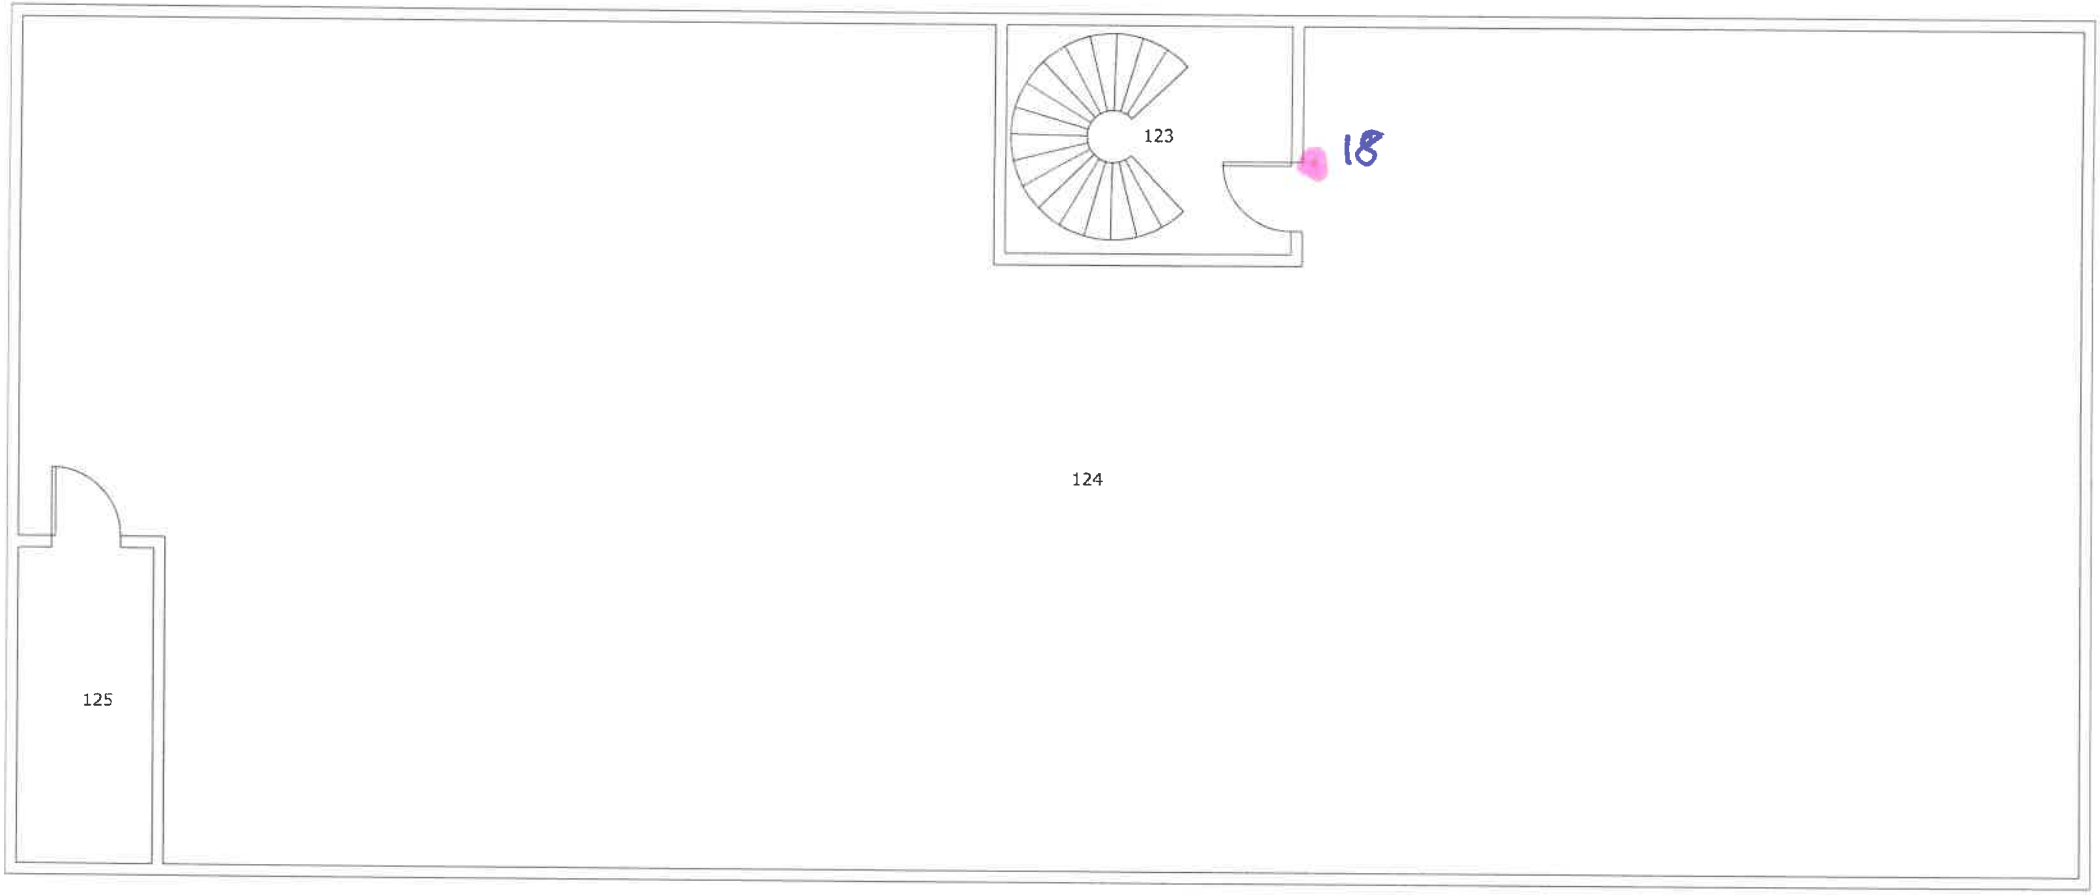

3.5a1