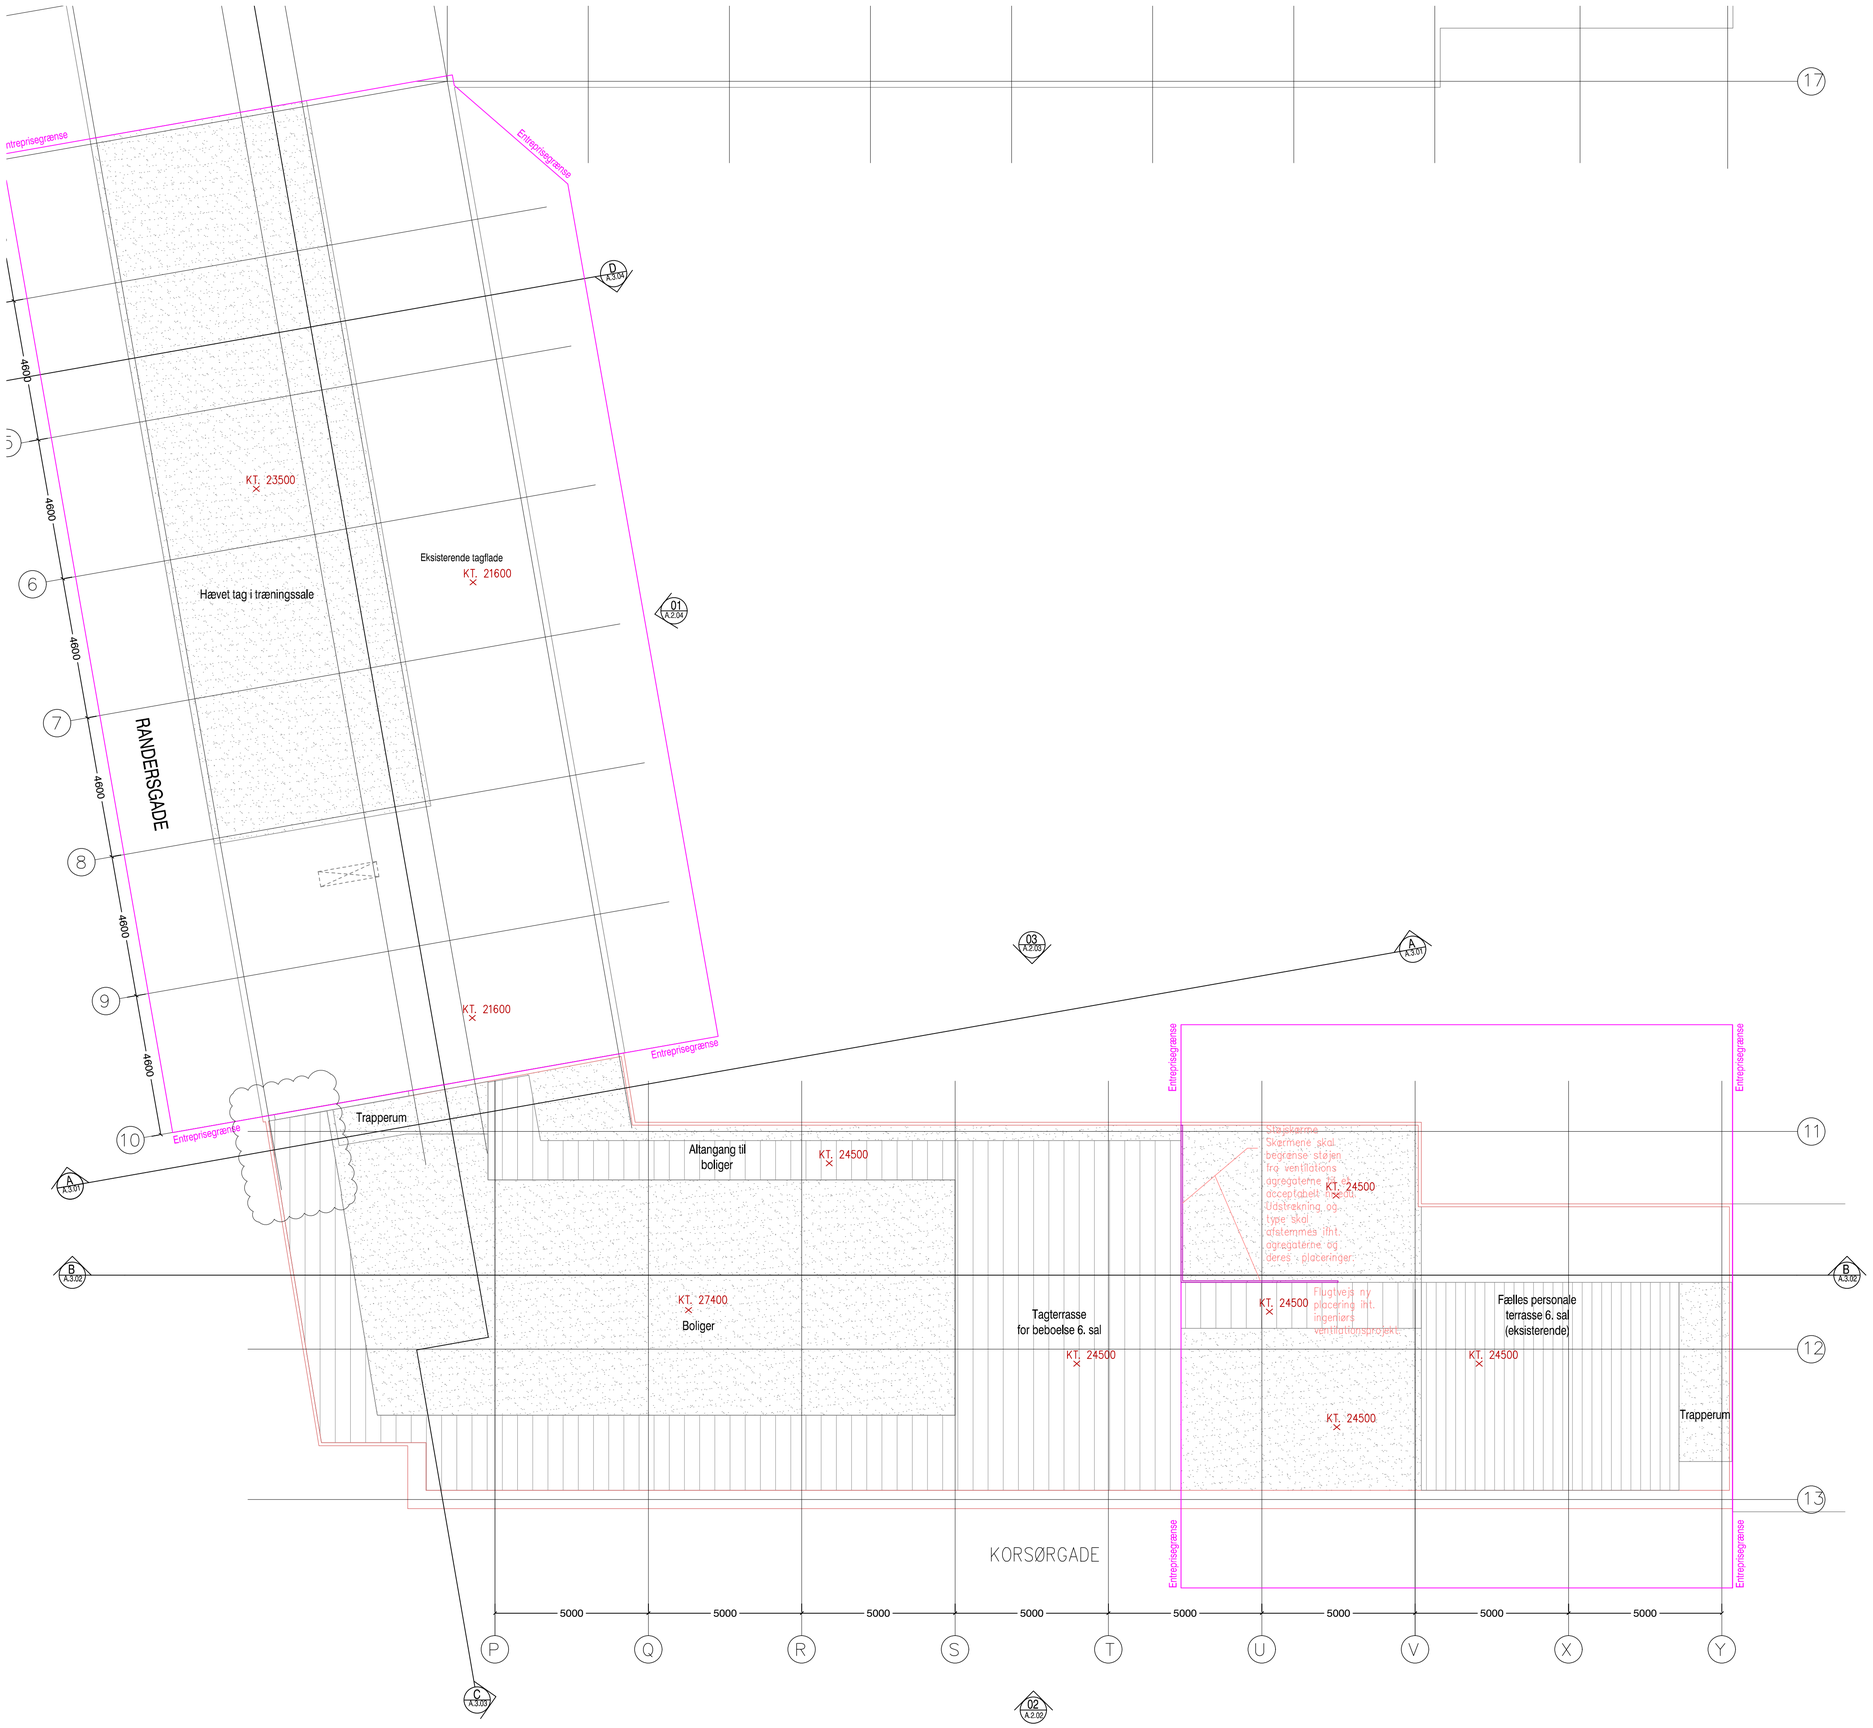

XX-X.XX — Eksisterende dør der bevares
Renoveres iht. dørskema

XX-X.XX — Ny dør i nyt murhul,
dør iht. dørskema

Ny foldevæg. Udføres som tophængte, centerhængte, hvor ikke andet er anført. Foldevægge monteres iht. leverandørens montageanvisning og udføres om muligt i fuld etagehøjde, min. 2300 mm højde. Parkering som angivet på tegning. Brand og lydkrav som angivet på tegning. Foldevæg ml. træningssale skal være slagfaste. Udføres som Deko FV eller tilsvarende.
Farve iht. farveskema. Længde måles på stedet. Opdeling af foldeelementer iht. leverandør.

Ny Indvendig gipsvæg, typer som angivet:

XX

T1 — 120 mm, 48 db, EI60 A2-s1,d0 (BS60)

T2 — 145 mm, 52 db, EI60 A2-s1,d0 (BS60)

Gipsvægge udføres med 2 lag gips på stålregel-skelet i system som knauf danogips. Vægge monteres iht. leverandørens montageanvisning og udføres i fuld etagehøjde. Skal klargøres for malerbehandling.
Der monteres underlag for sanitets- og installationsgenstande mm. iht. leverandørens anvisninger. Alle udadgående hjørner/kanter skal hjørnebeskyttes. I rum, hvor der er vådrumszone skal der vådrumssikres og vådrumsplader benyttes.

Fodlister og gerigter udføres i massivt træ 15x65 mm sømmet/boret og malerbehandlet. Sømhuller skal udspartles før malerbehandling.
Grundes inden opsætning og færdigbehandles efter opsætning.

Systemleverance i h.t. ingeniørprojekt for elevator

Eksisterende væg der bevares, malerbehandles.
Farve iht. farveskema.

VX — Nyt glasparti i nyt murhul, glasparti iht. vinduesskema.

Eksisterende glasparti der bevares, malerbehandles.
Farve iht. farveskema.

Nyt glasparti i facade, iht. tegning se tegningsliste for nr.

Vægge der nedrives. Vægge nedrives i fuld højde.
Arbejdet omfatter alt hvad der måtte sidde på væggen af lister, fodlister, sanitet etc. Det angivne omfang er vejledende.

Dør der nedrives. Arbejdet omfatter hele døren inkl. dørblad, karm, gerigter, besætning og hvad der måtte anses for værende tilhørende døren. Det angivne omfagn er vejledende.

Eksist. dør-/vindueshul der blændes.
Blænding som omgivende væg eller tilsvarende lyd og brand niveau. Overflade plan med omgivende væg og forberedt for malerbehandling. Det angivne omfang er vejledende.

N

AH	AKTIVITETSHUSET
SK	SYGEPLEJEKLINIK
TC	TRÆNINGSCENTER
FC	FOREBYGGELSESCENTER
FL	FÆLLES RUM / AREALER
E1	ELEVATOR 1, EKSISTERENDE
E2	ELEVATOR 2, EKSISTERENDE
E3	ELEVATOR 3, EKSISTERENDE M
E4	ELEVATOR 4, NY ETABLERES
ET	ELTAVLE
FS	FALDSTAMME, eksisterende
HL	HÅNDLISTE, iht. bygningsdelst se tegningsliste for nr.
HS	HÆVE–SÆNKE VASK iht. rumte se tegningsliste for nr.
HV	HÅNDVASK ETABLERES iht. ru se tegningsliste for nr.
HV E	HÅNDVASK EKSISTERENDE
UV	UDSLAGSVASK
KF	KRYDSFELT
TV	TAGVAND, FALDSTAMME
UDL	Udlejnings etage
VÆ	VÆRN ETABLERES, iht. bygnings se tegningsliste for nr.
GA E	GULVAFLØB, EKSISTERENDE
GA	GULVAFLØB, ETABLERES

Eksisterende toiletter
Sanitet som eksisterende. Sanitetsudstyr udskiftes, hvor det er nødvendigt.

Malerbehandling:

Alle overflader males så de fremstår mættede, dækkede og ensartede og udføres iht. MBK's anvising iht. det pågældende underlag med høje æstetiske udfaldskrav.

Afsluttende fugning med acryfluge udføres mod alle tilstødende bygningsdele for malerbehandling.

Nye gipsvægge/indækning:
- slibning
- 1 gang pletspartling med sandspartelmasse
- grunding med pladstgrunder
- opsætning af glasfilt i vævklæber
- 1 gang plastvævfylder
- 3 gange akryl plastmaling glans 10.

Eksisterende vægge:
Vaskes, huller og skader pletspartles, slibes og malerbehandles iht. underlaget.

Eksisterende flisevægge:
Vaskes, overspartles til plan overflade, grundes filtes malerbehandles.

Fast inventar:
Der henvises til rumtegninger.

- Tegningerne er digitaliseret efter gamle tegninger.
- Alle koter og mål skal kontrolleres på stedet.
- Alle korter angives i henhold til aktuel vandstand.
- Følg Bygningsreglementet 10 (BR10) samt den Danske Standard (DS), hvor intet andet er angivet.
- Skalér ikke tegningen.
- Hvis der forekommer uoverensstemmelser mellem tegninger, giv da venligst arkitekten besked herom.

Rev.	Dato	Emne
A	20–03–2015	Tagplan tilpasset eksist. forhold

DATEA
● DATEA AS
Lyngby Hovedgade 4, 2800 Kgs. Lyngby
Tlf.: +45 45 26 01 02, Fax: +45 45 26 02 89
WWW.datea.dk

Tegningsnummer
35089 256
A.1.09 A

Ejendom: 35089 Vordingborggade 18–22,
Randersgade 60, Korsørgade 3

Emne: Plan
Tag

Ejer:	DADES A/S				
Matr.nr.:	866	Dato:	13–02–2015	Mål:	1:100 / A1
Sag:	Sundhedshuset IBØ	Sign.:		Godkendt:	X
Filnr.:	T–A–1–ET–08.dwg 09–12–2015 14:31:32	x–ref.:		Filansvarlig:	X